


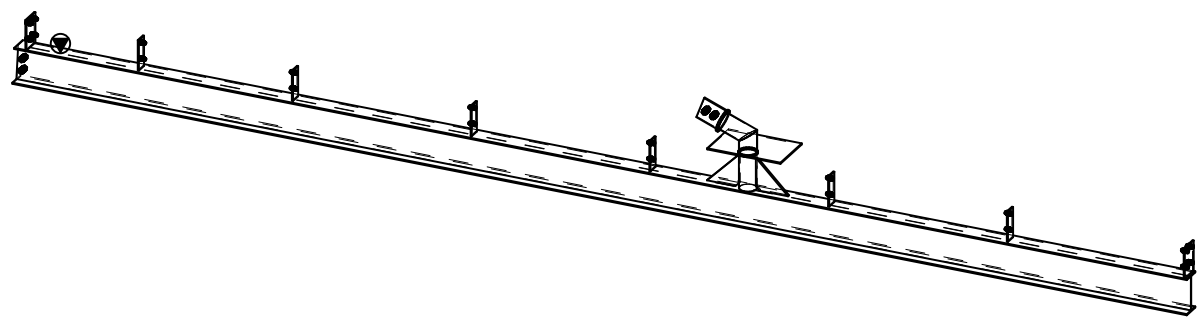
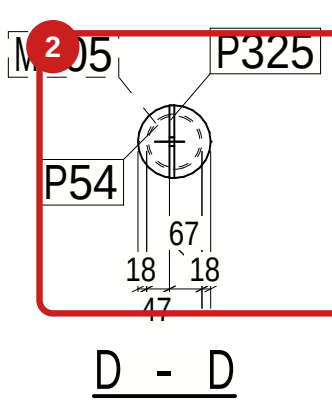
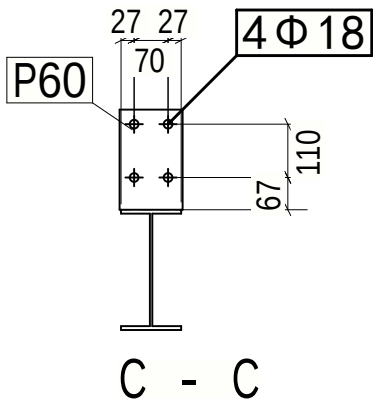


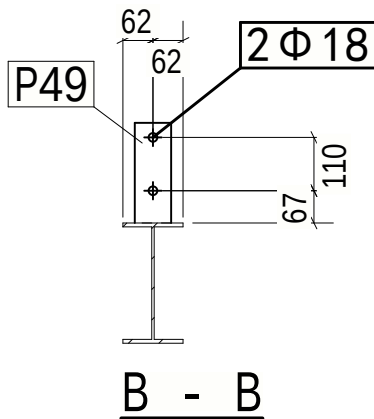


ISOMETRIC VIEW

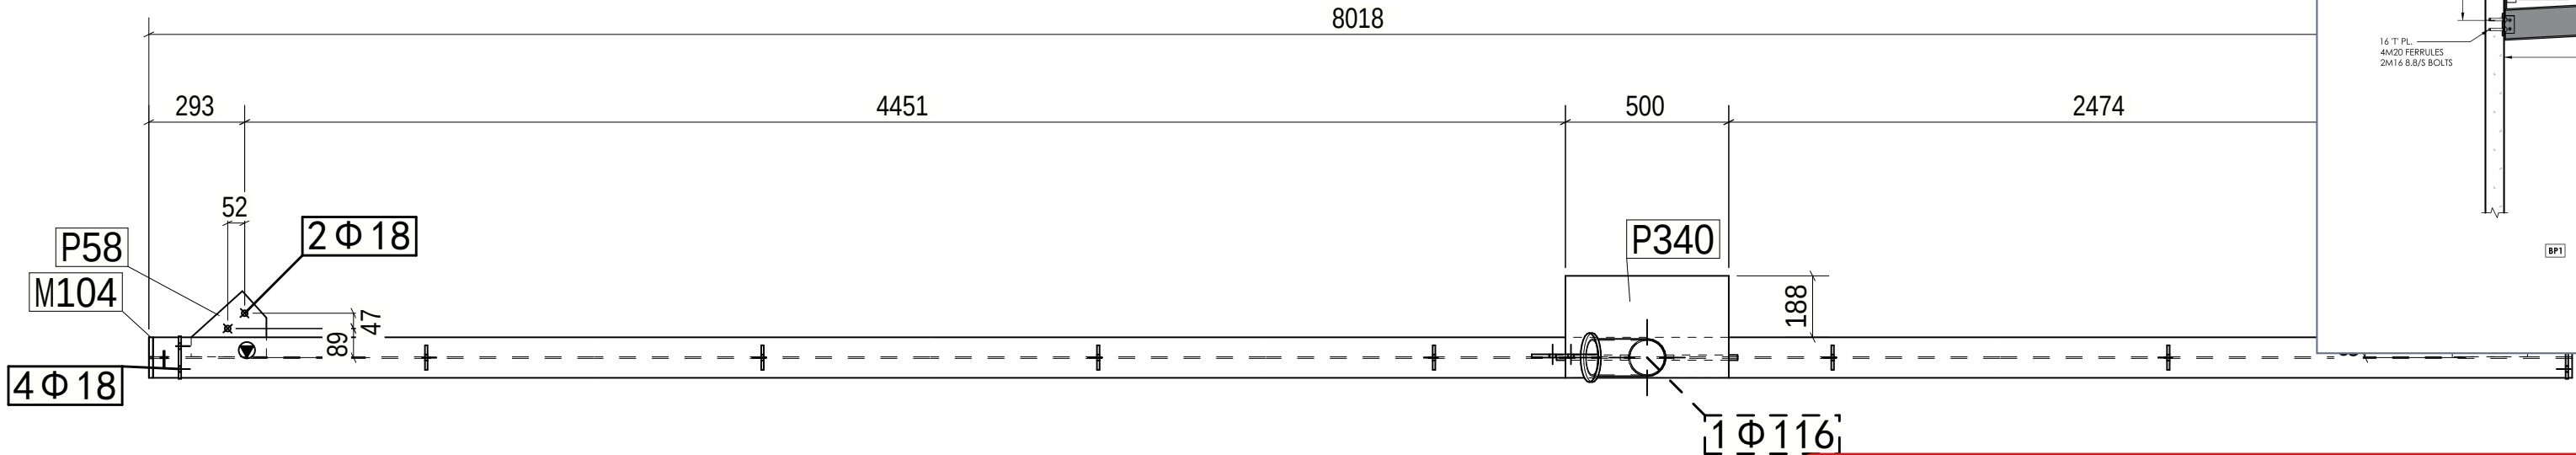

MATERIAL LIST						
Mark	Qty.	Description	Length	Grade	Part(kg)	Total(kg)
M104	1	250UB25.7-HN248*124*5*8	8018	Q355B	201.3	201.3
M105	1	CHS114*4	219	Q355B	2.3	2.3
M347	1	CHS114*4	398	Q355B	4.3	4.3
P49	6	PL8*75	206	Q355B	1.0	5.8
P52	2	PL16*220	220	Q355B	6.1	12.2
P54	1	PL10*150	150	Q355B	1.8	1.8
P58	2	PL10*201	230	Q355B	3.6	7.3
P60	2	PL8*130	206	Q355B	1.7	3.4
P325	1	PL10*160				
P340	1	PL8*312				
Totals for ONE						
Combined Total for A						

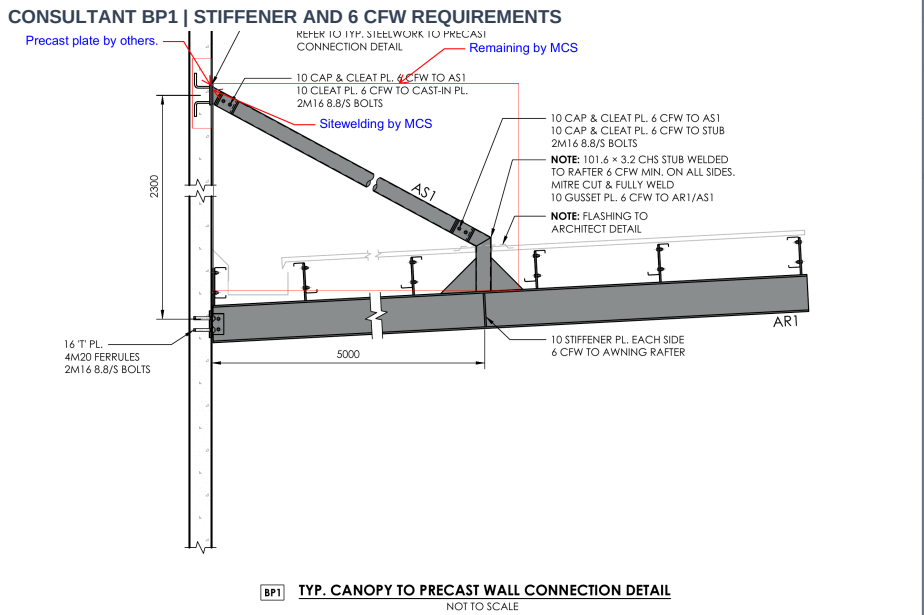

A - A

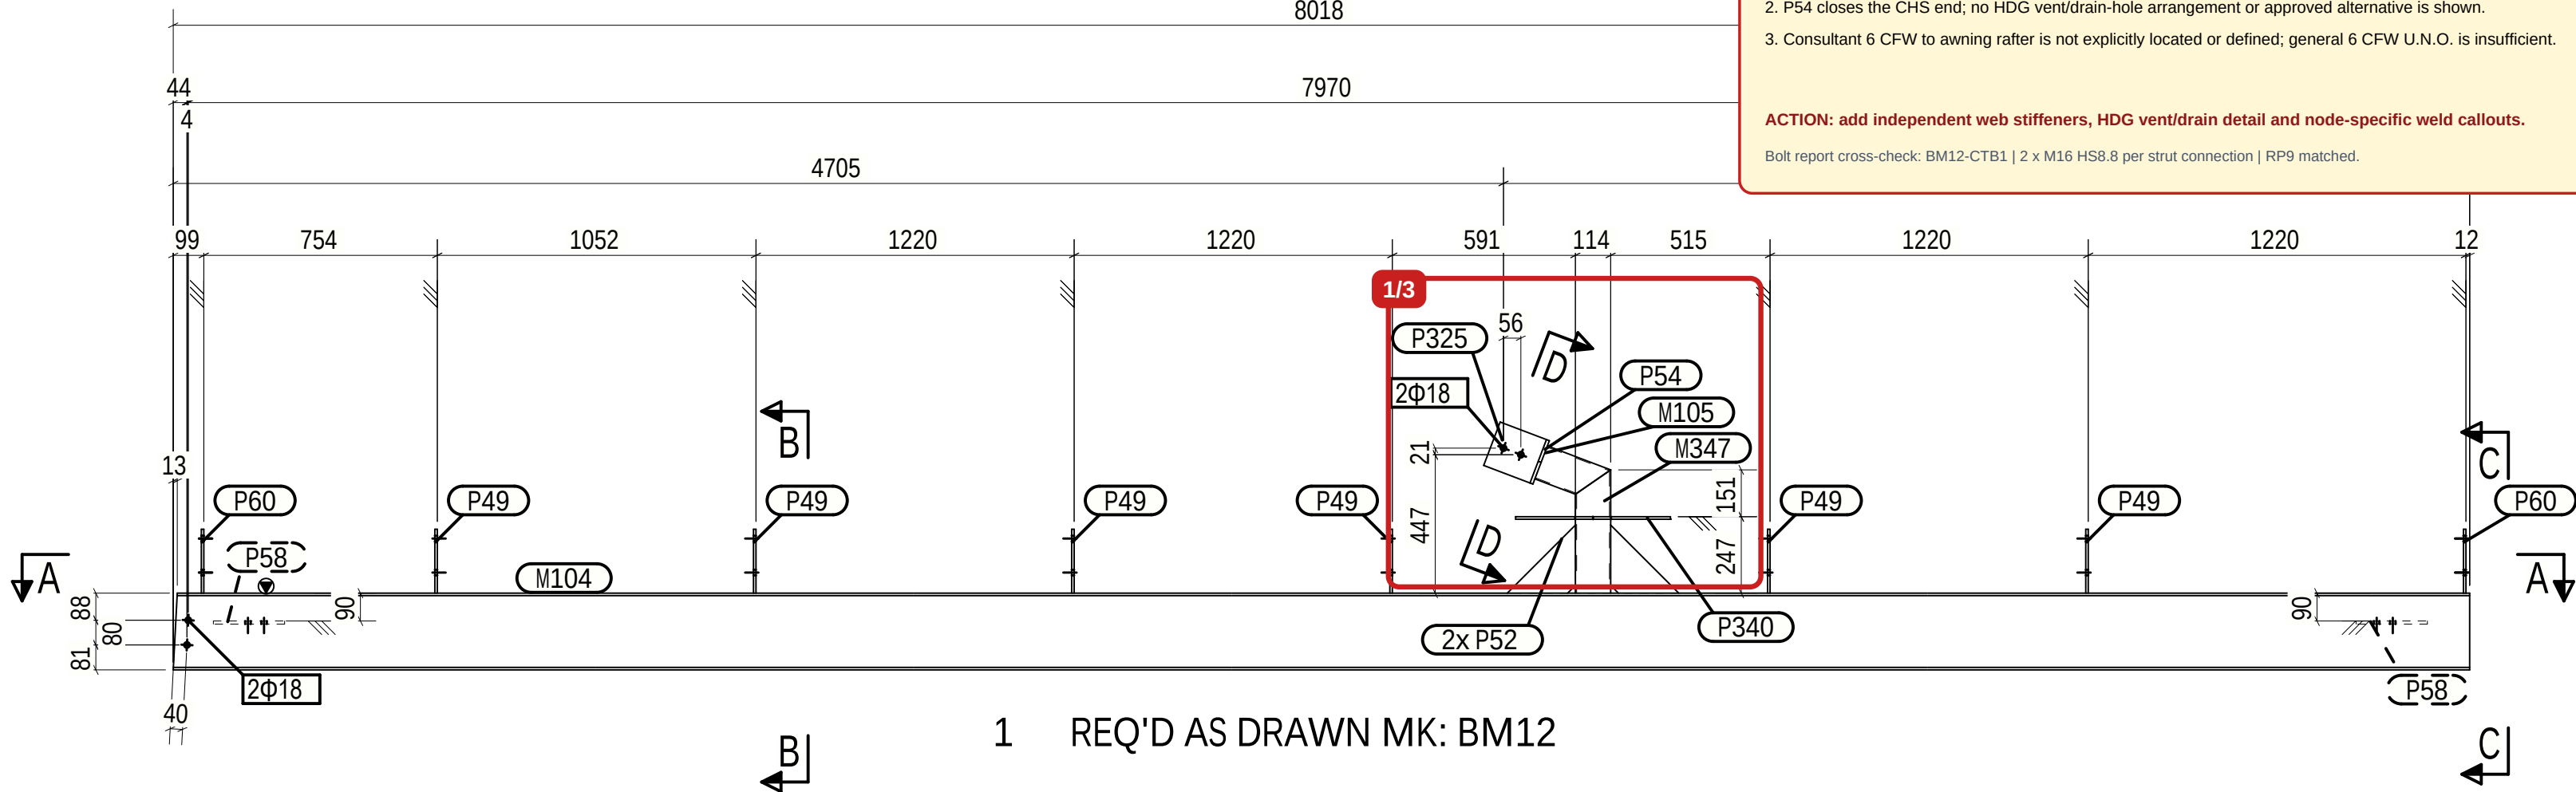

1 REQ'D AS DRAWN MK: BM12

FINSH: HDG

ISSUES BM12-01 / 02 / 03 | CENTRAL AWNING NODE

- 1. 10 mm stiffener plate EACH SIDE of the M104 web is not separately detailed; P52 is not the required stiffener.
- 2. P54 closes the CHS end; no HDG vent/drain-hole arrangement or approved alternative is shown.
- 3. Consultant 6 CFW to awning rafter is not explicitly located or defined; general 6 CFW U.N.O. is insufficient.

ACTION: add independent web stiffeners, HDG vent/drain detail and node-specific weld callouts.

Bolt report cross-check: BM12-CTB1 | 2 x M16 HS8.8 per strut connection | RP9 matched.

--	--	